



STARBOARD SOLAR HOME




COLORADO SUNWORKS BOULDER



**ARCHITECTURAL DESIGN:
CHRISTOPHER MELTON**

**SOLAR DESIGN:
PAUL SHIPPEE**

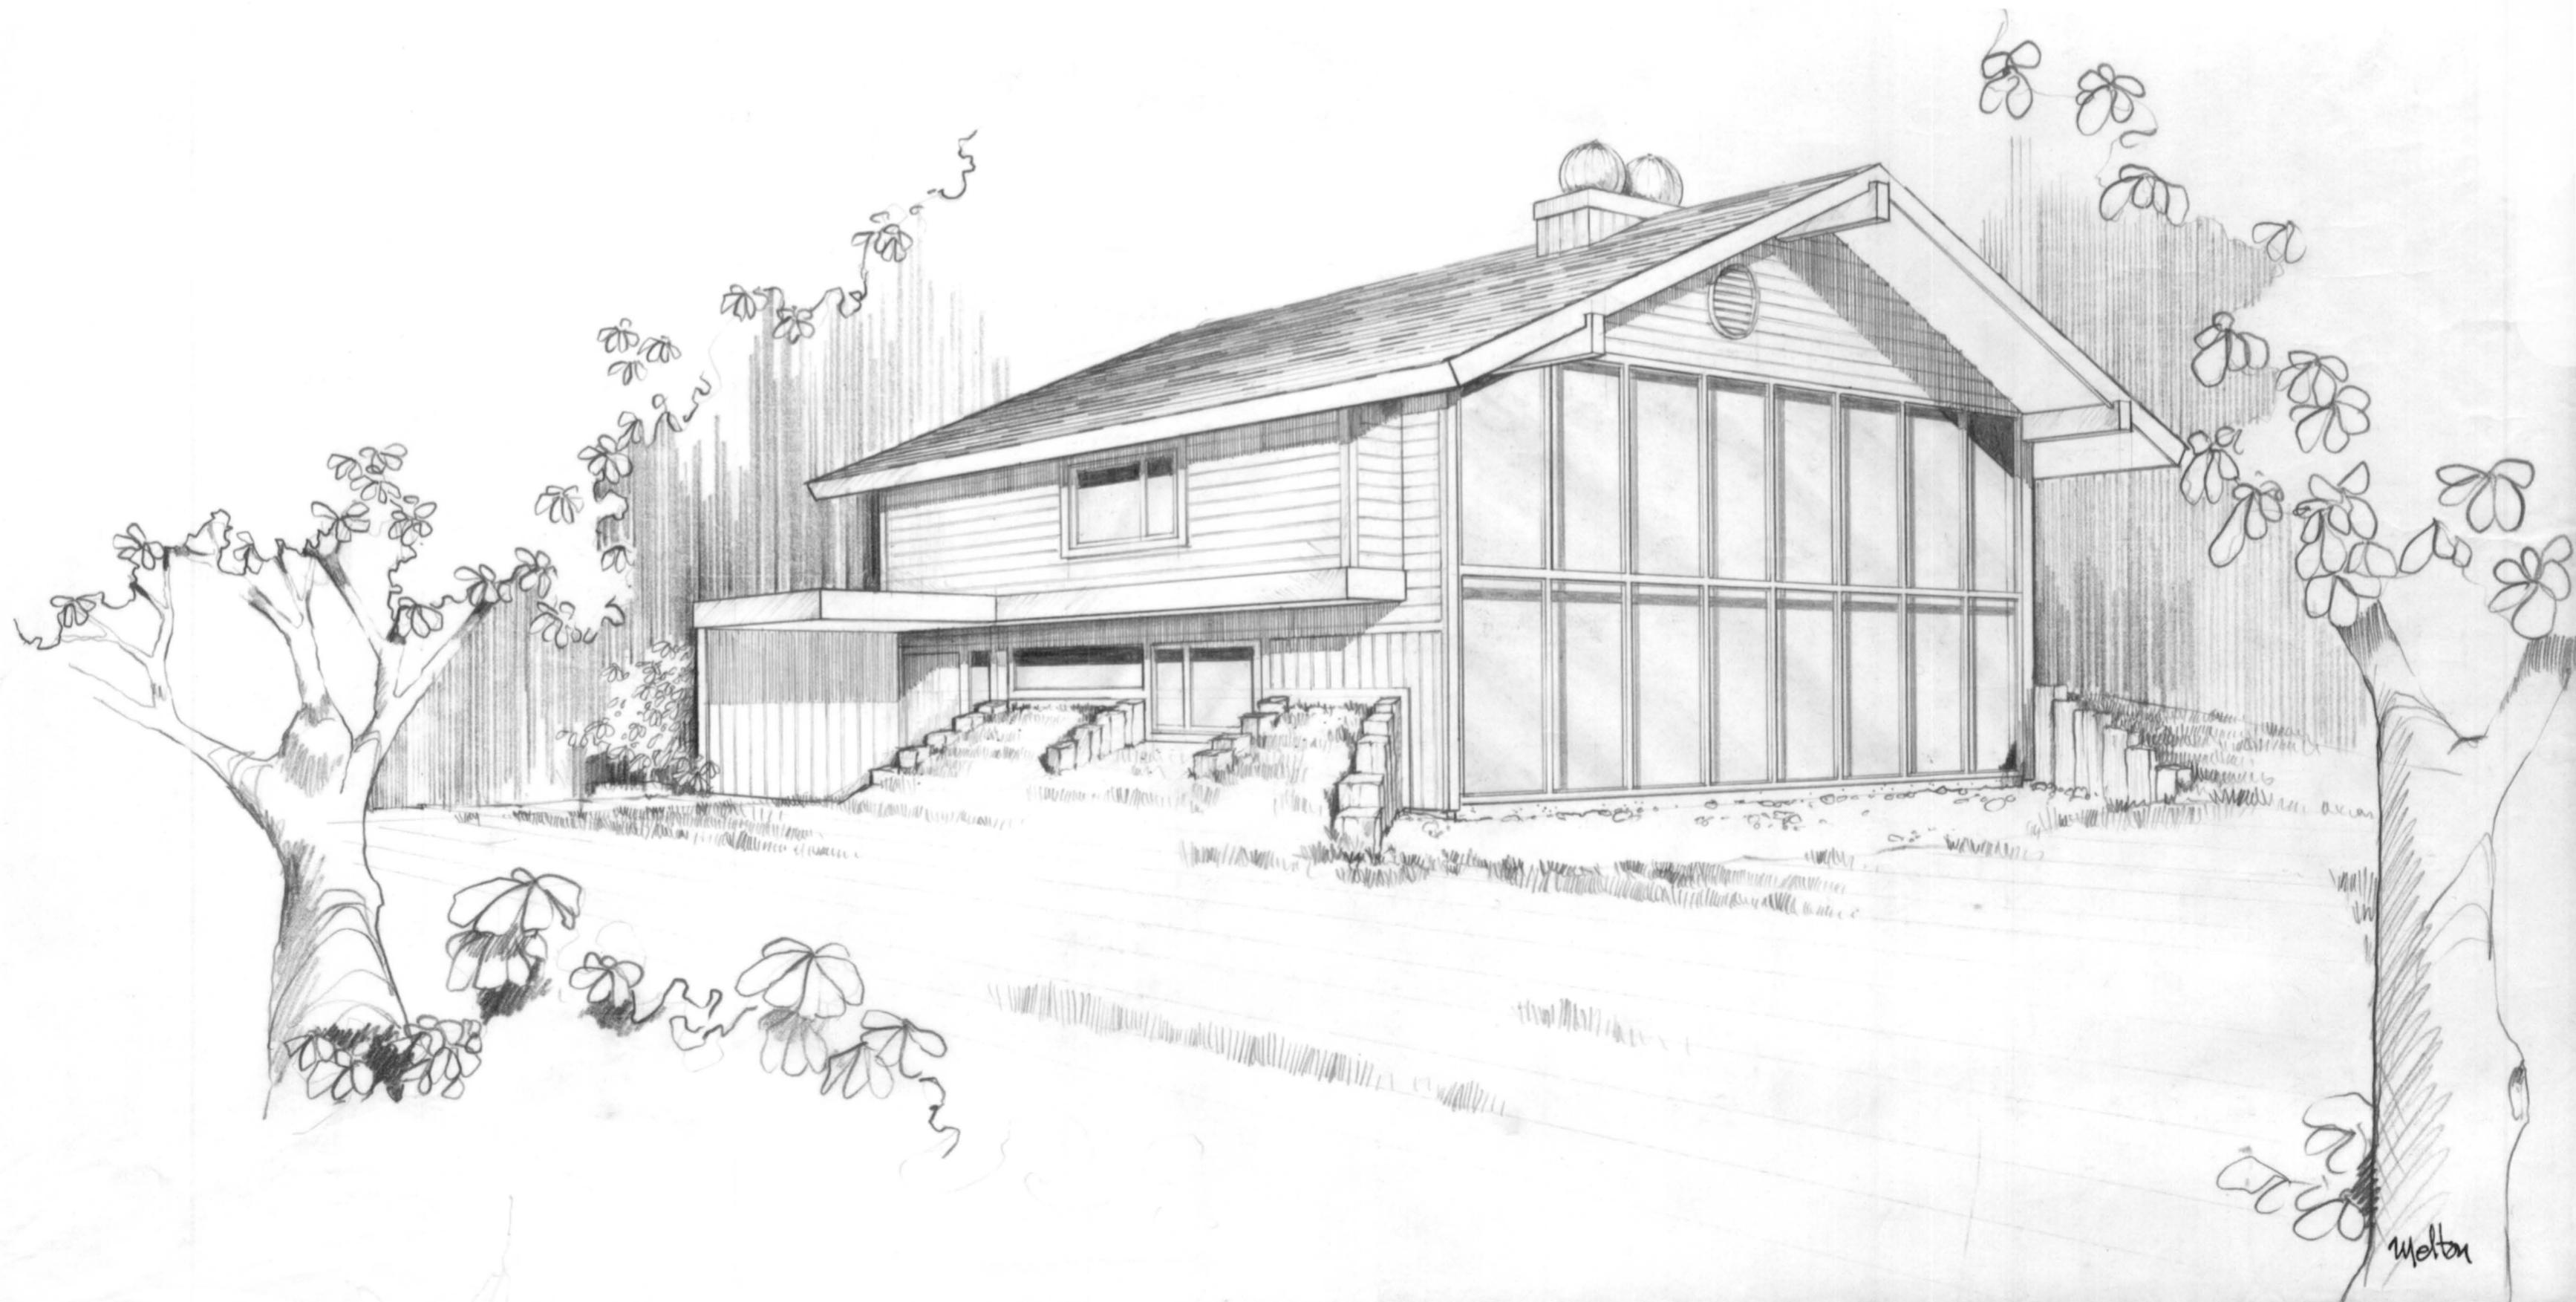

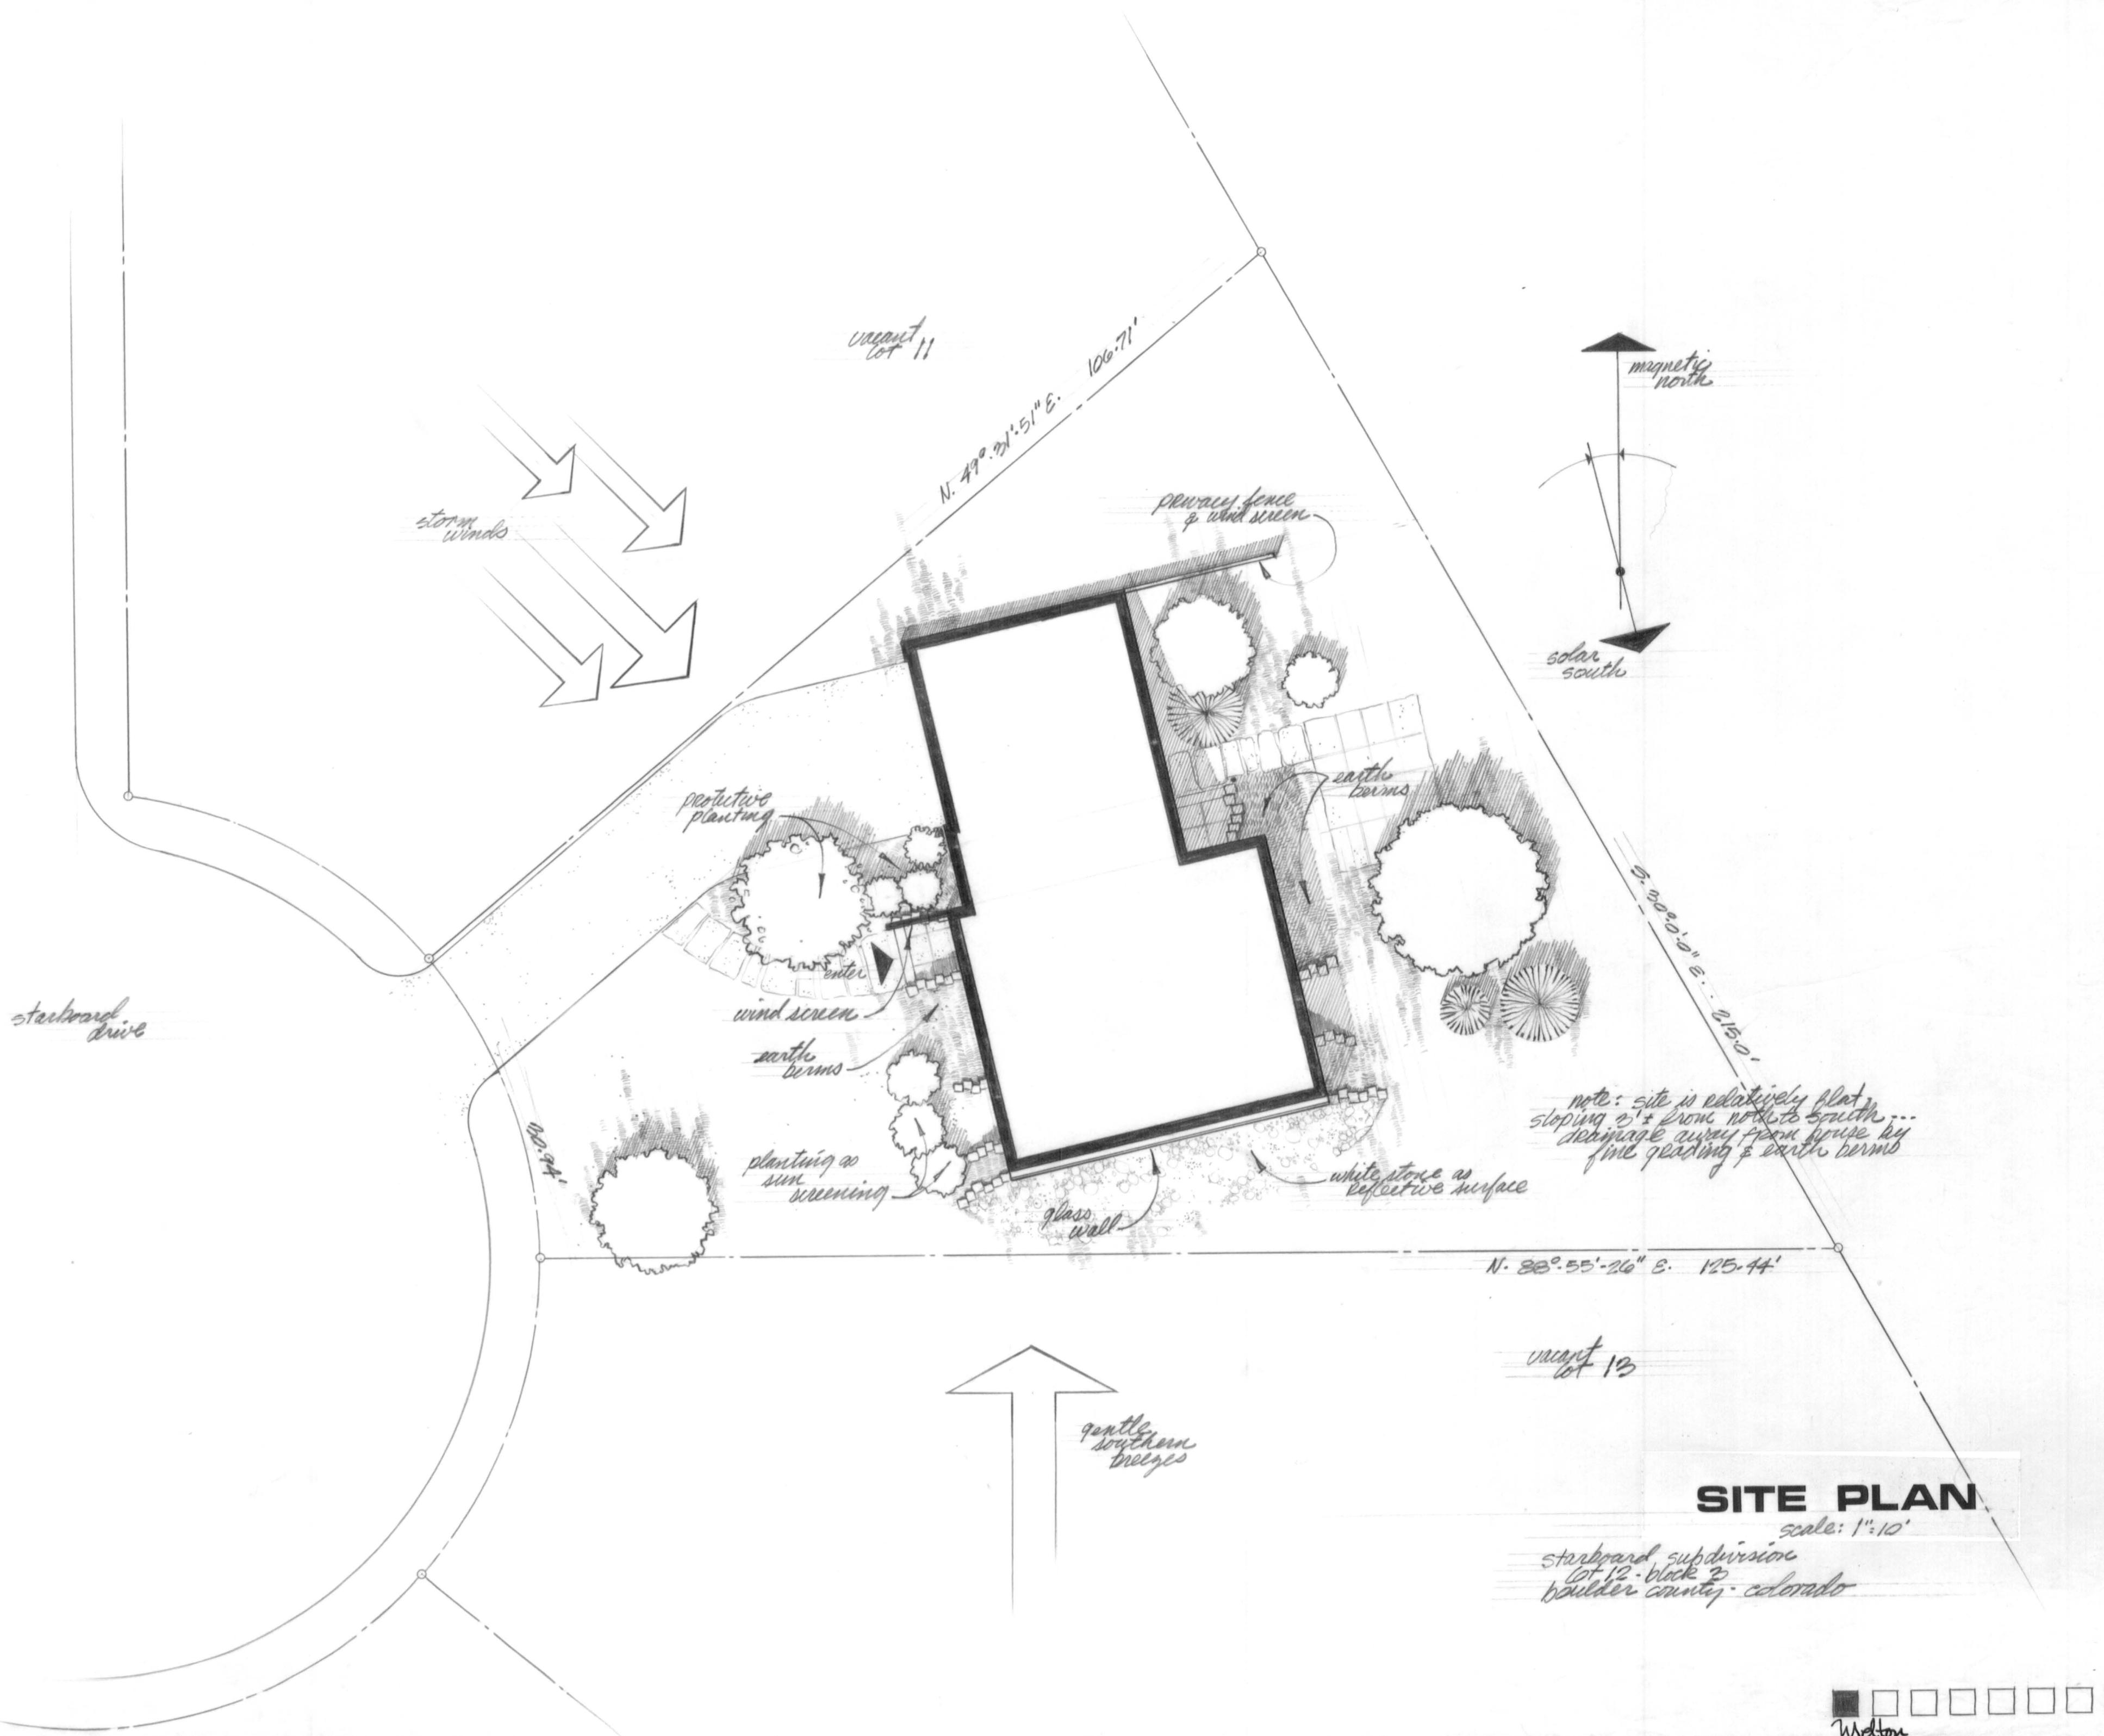


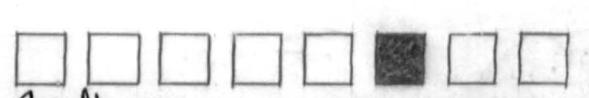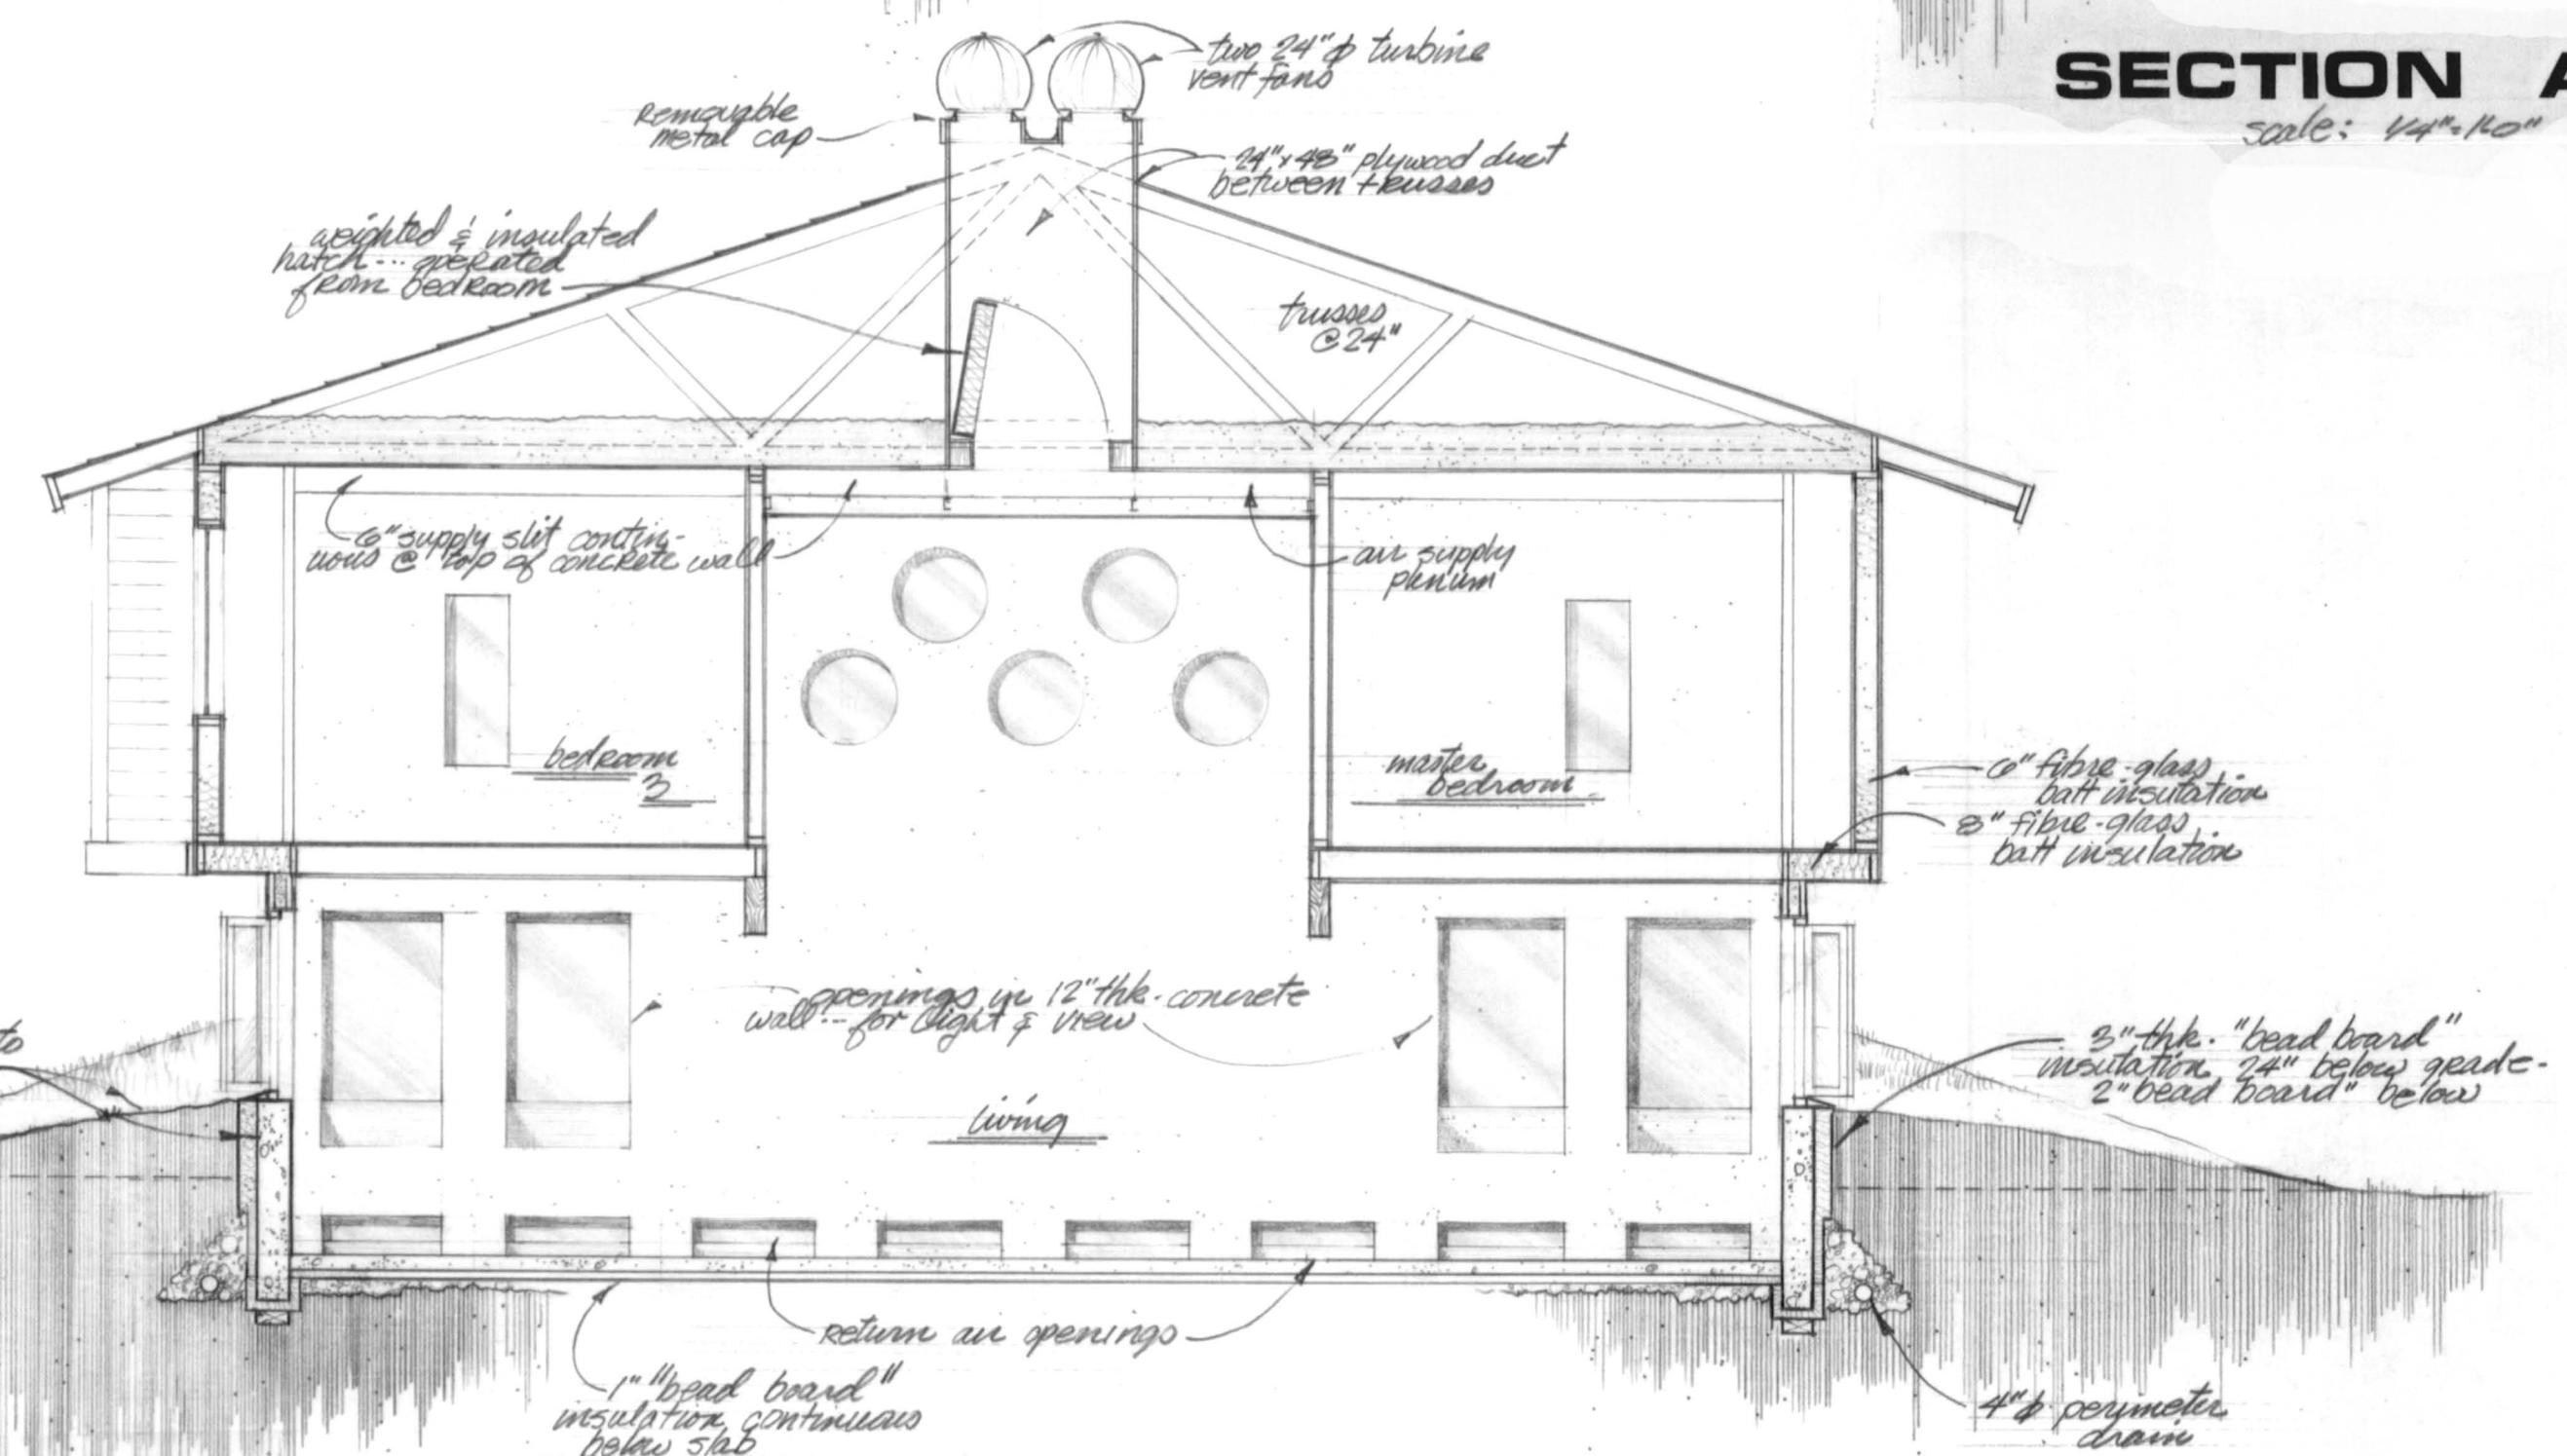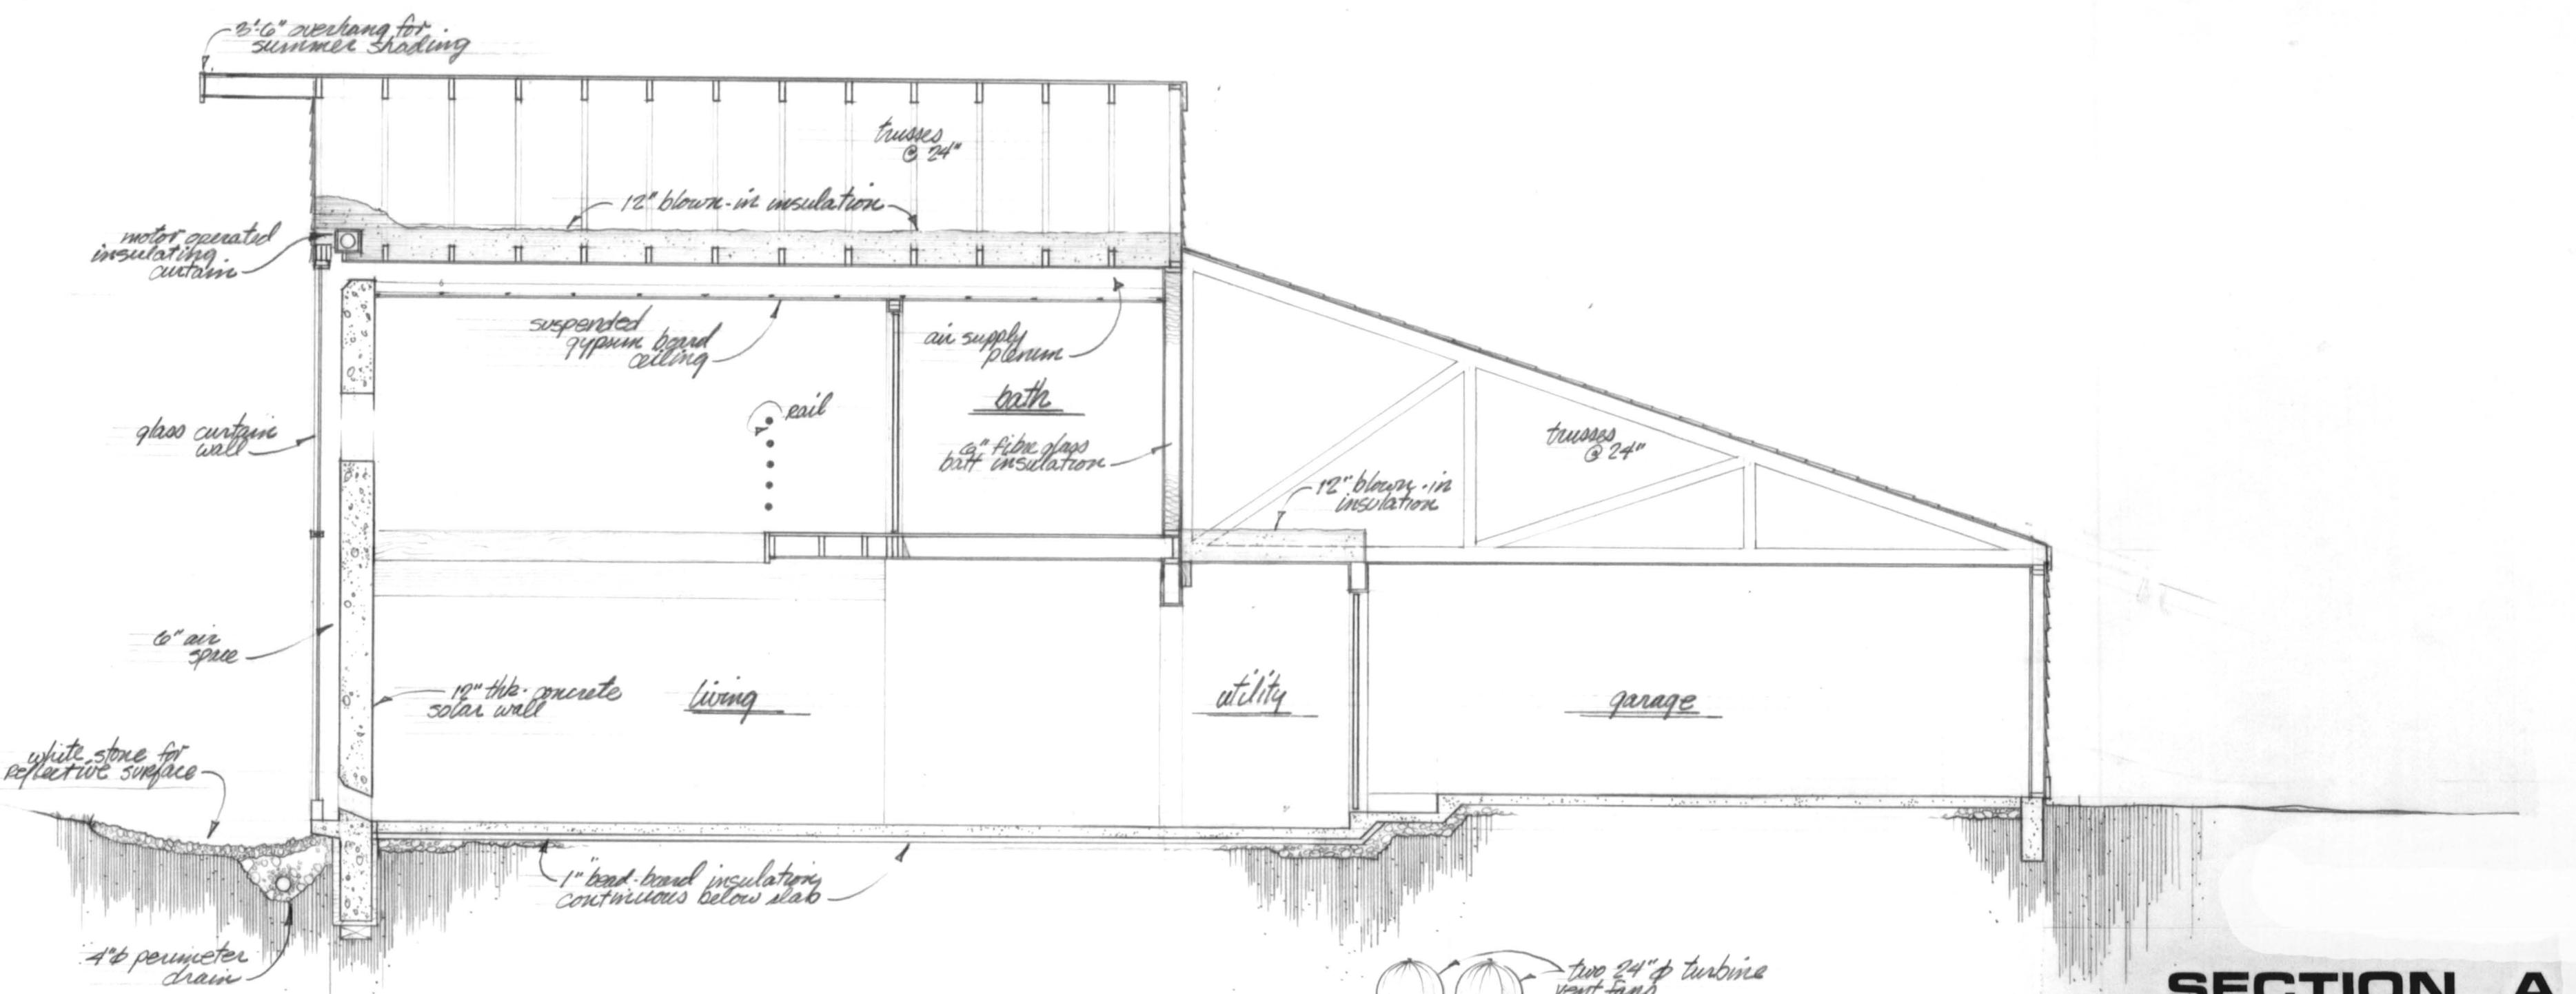


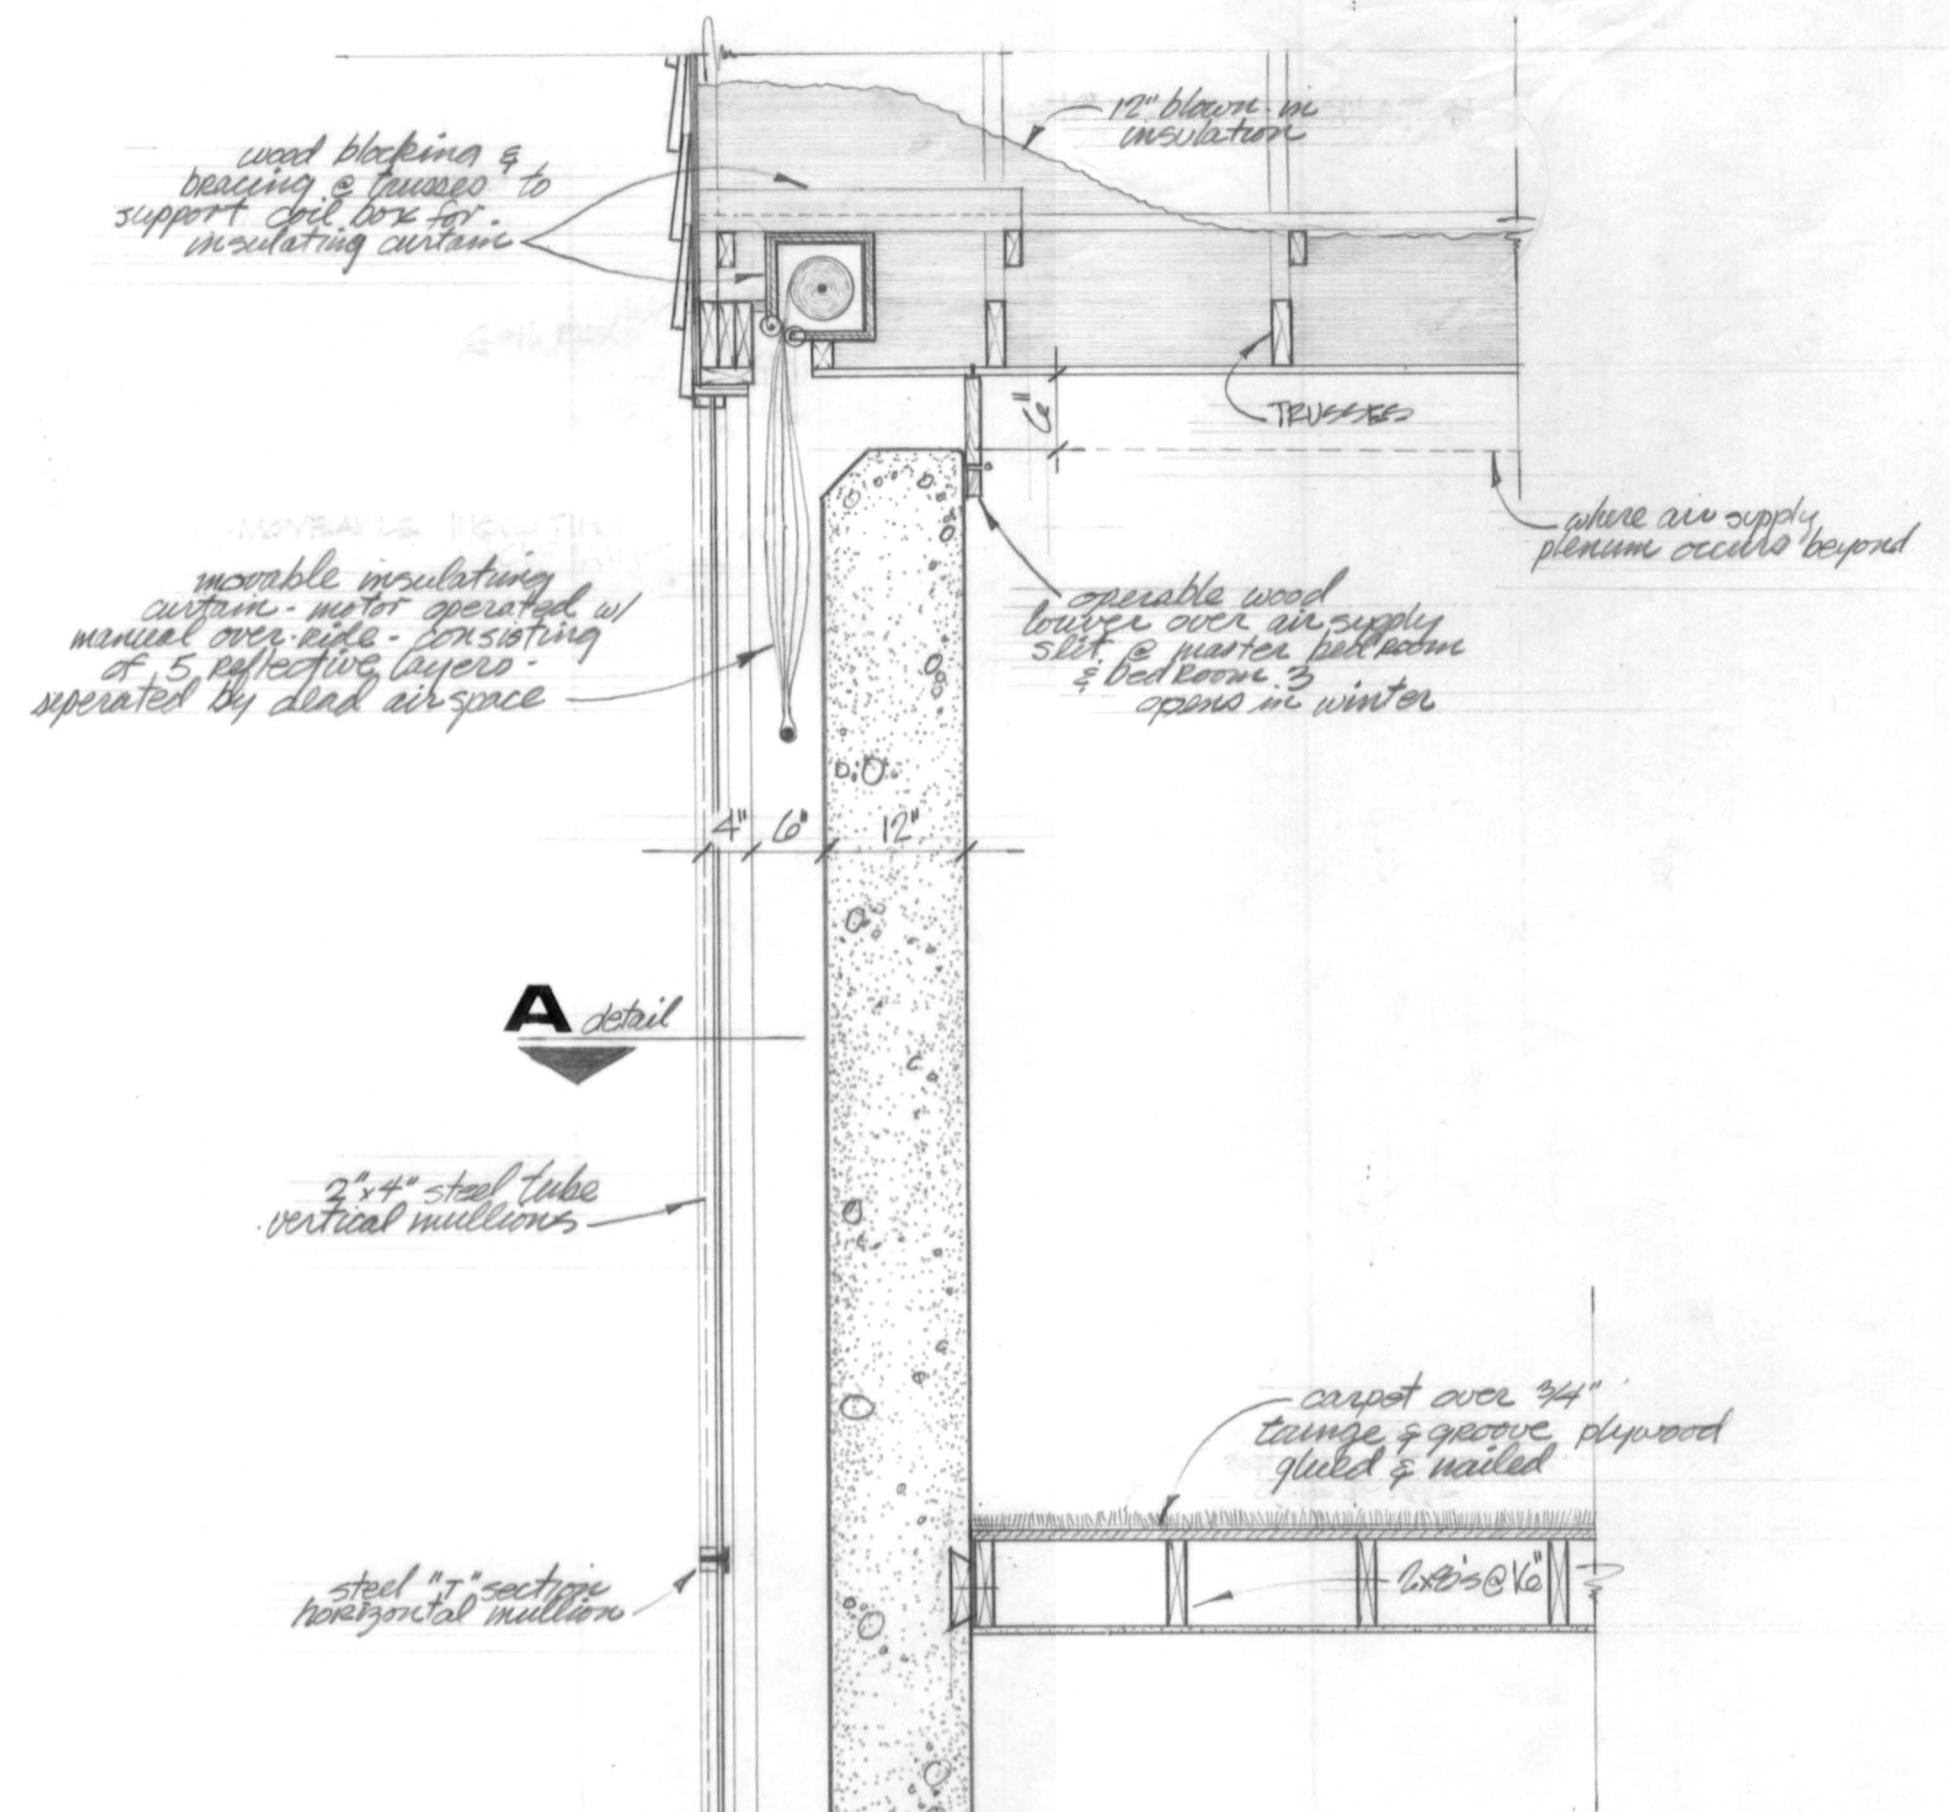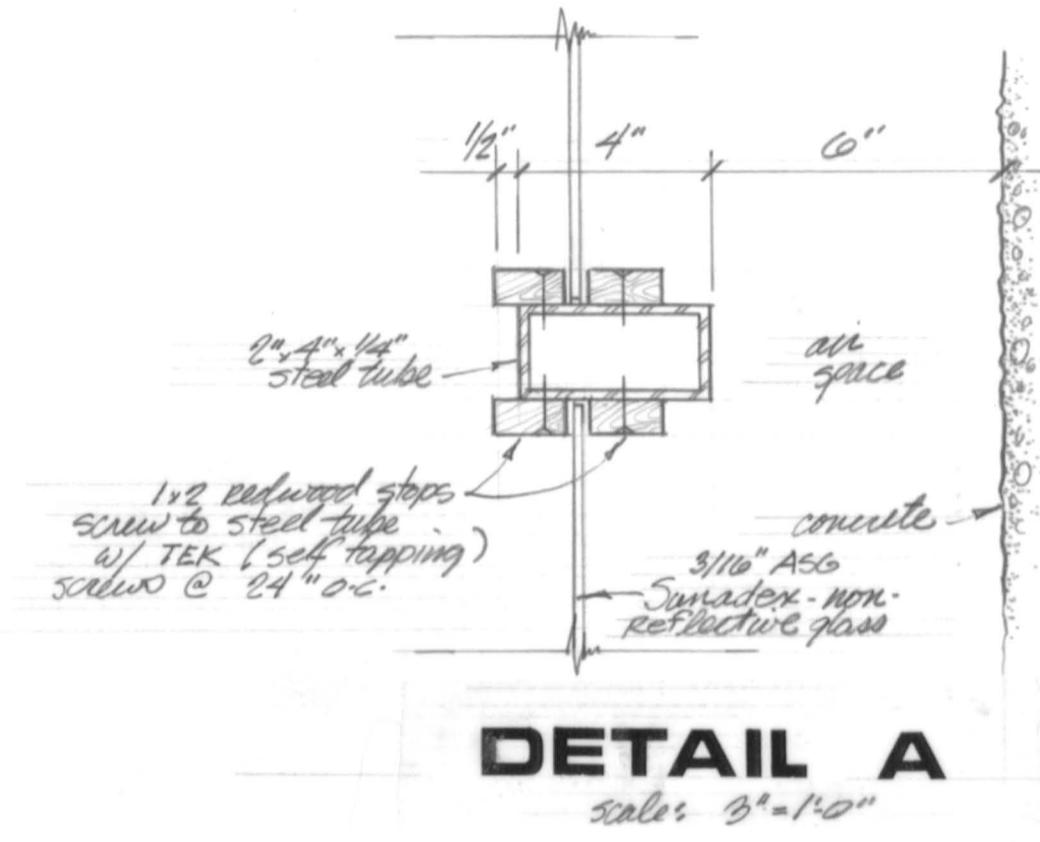

SOLAR WALL SECTION

scale: 3'-0" = 1'-0"


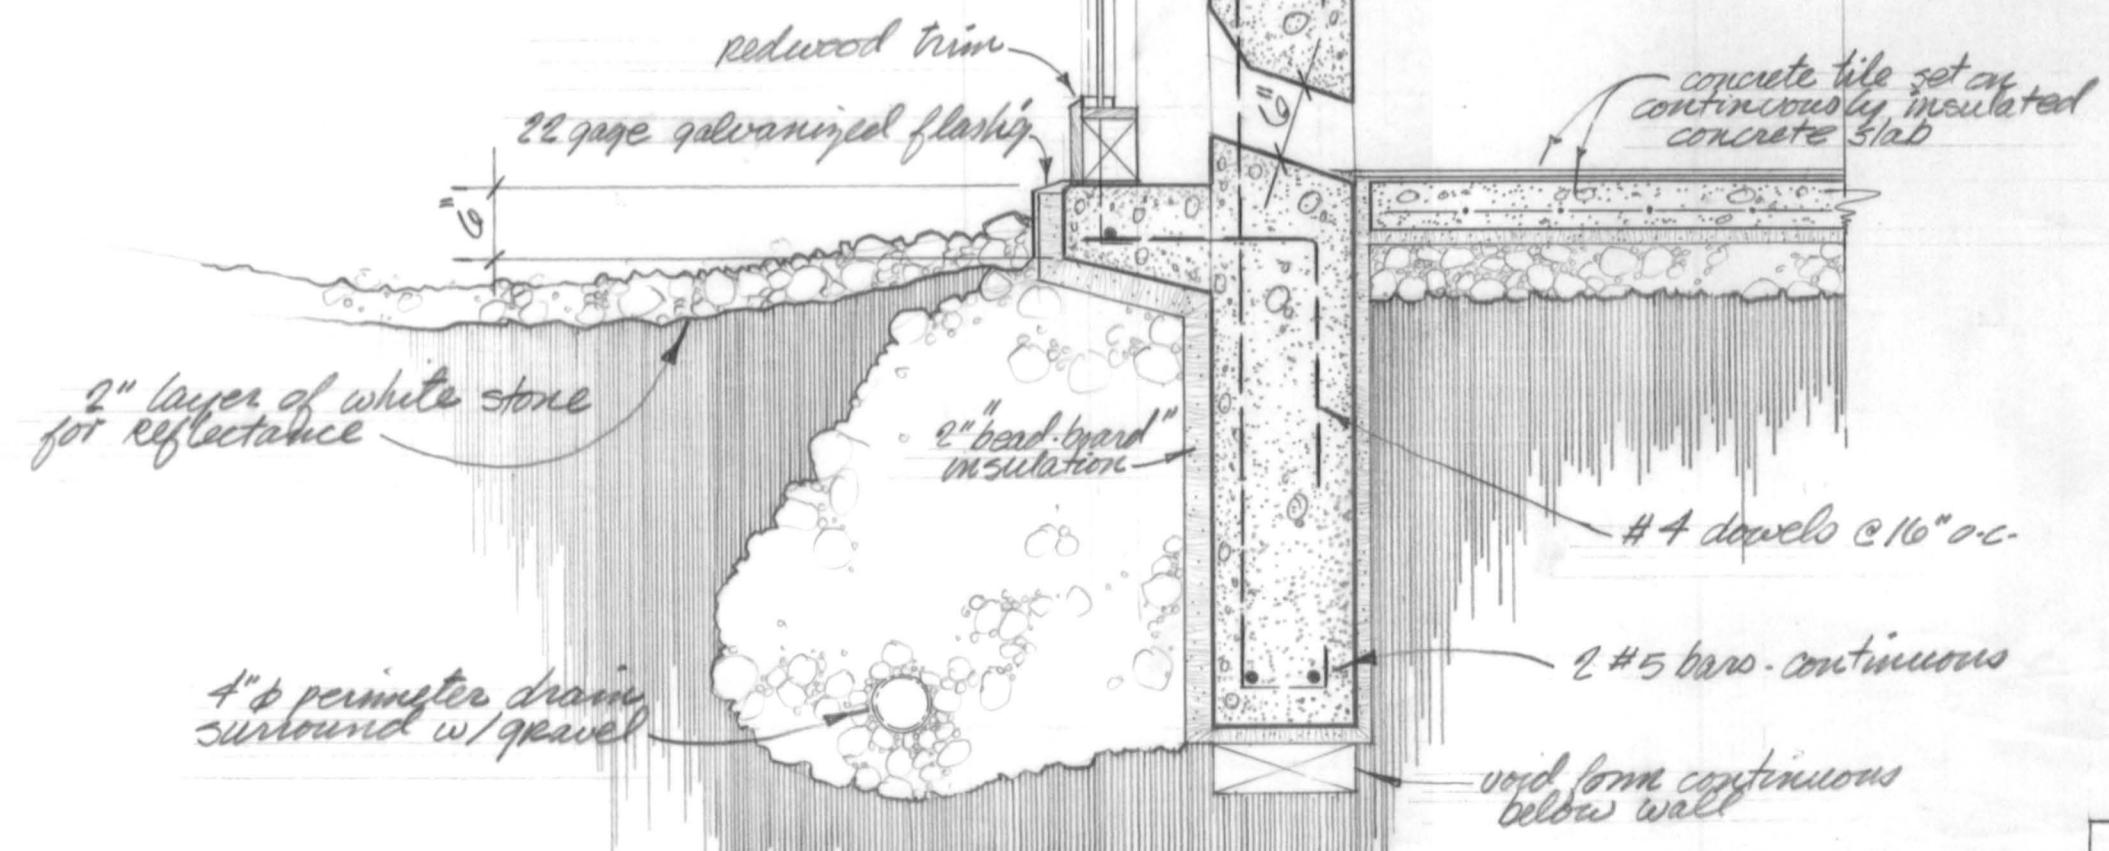


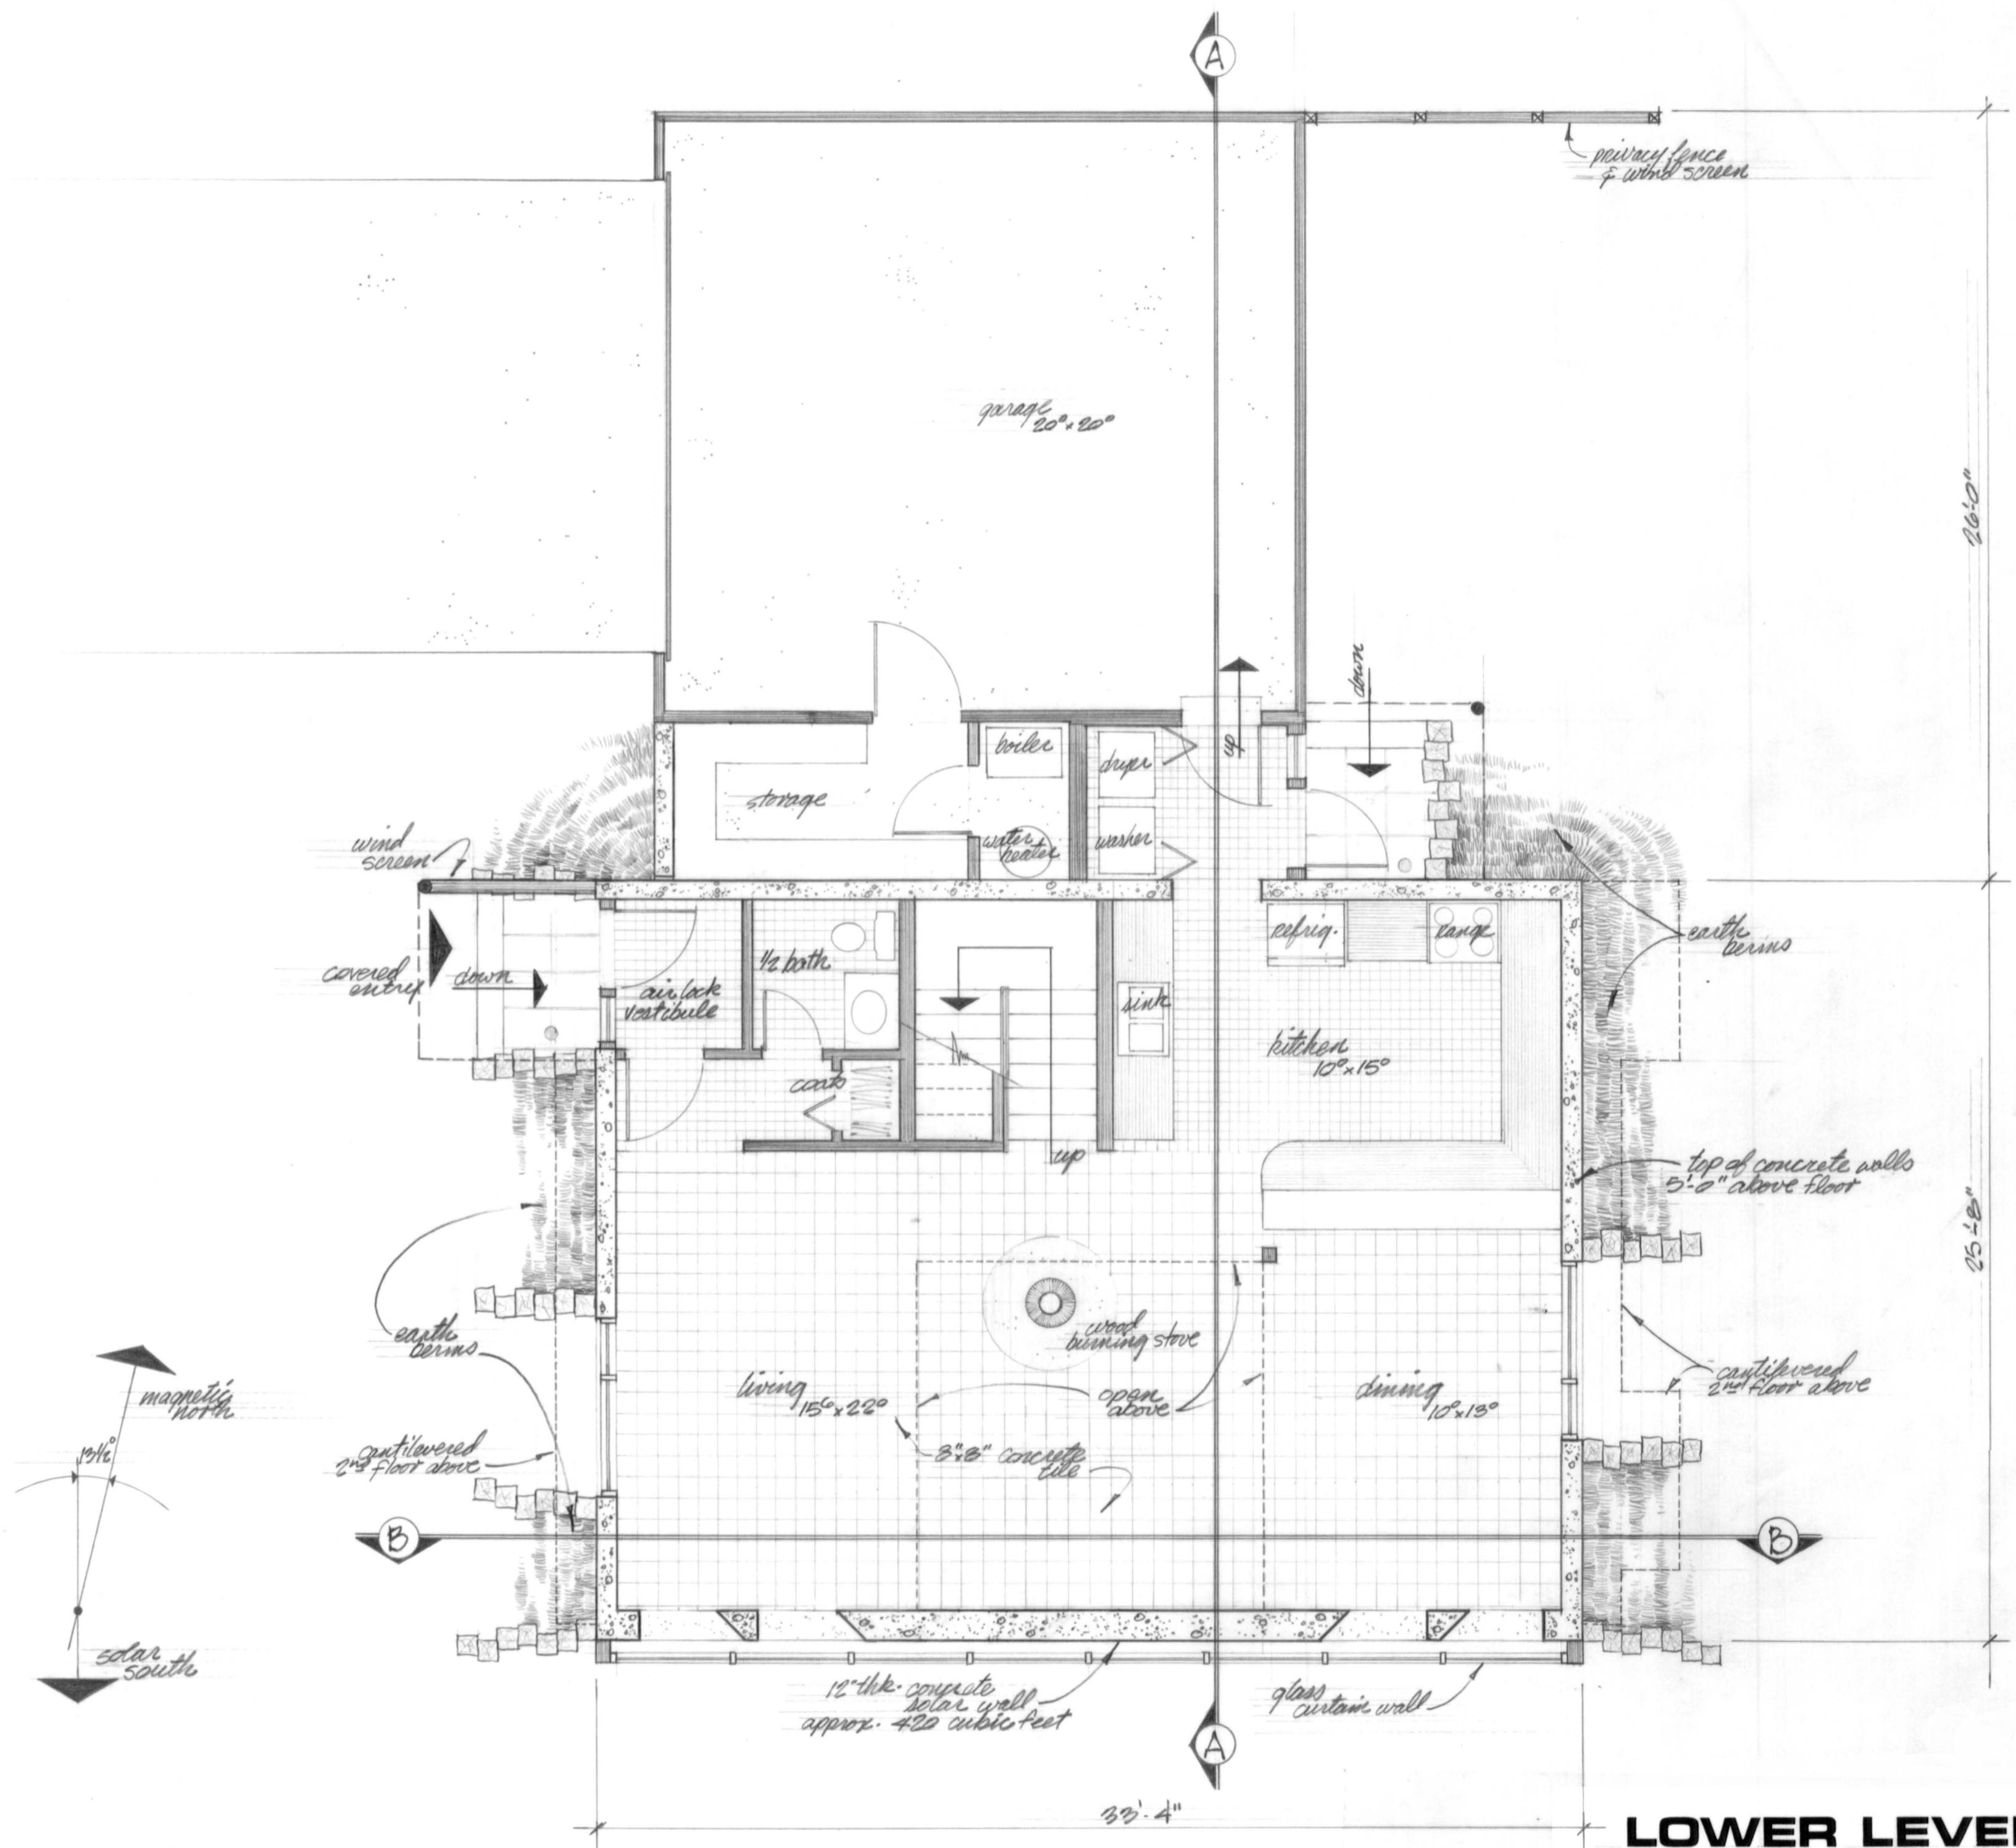

LOWER LEVEL PLAN

Scale: $14^{\circ} 10^{\prime \prime}$
 Lower level ... 808 sq. ft.
 Upper level ... 720 sq. ft.
 Total ... 1528 sq. ft.



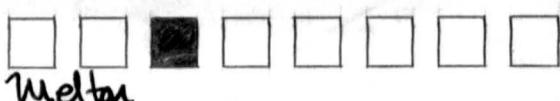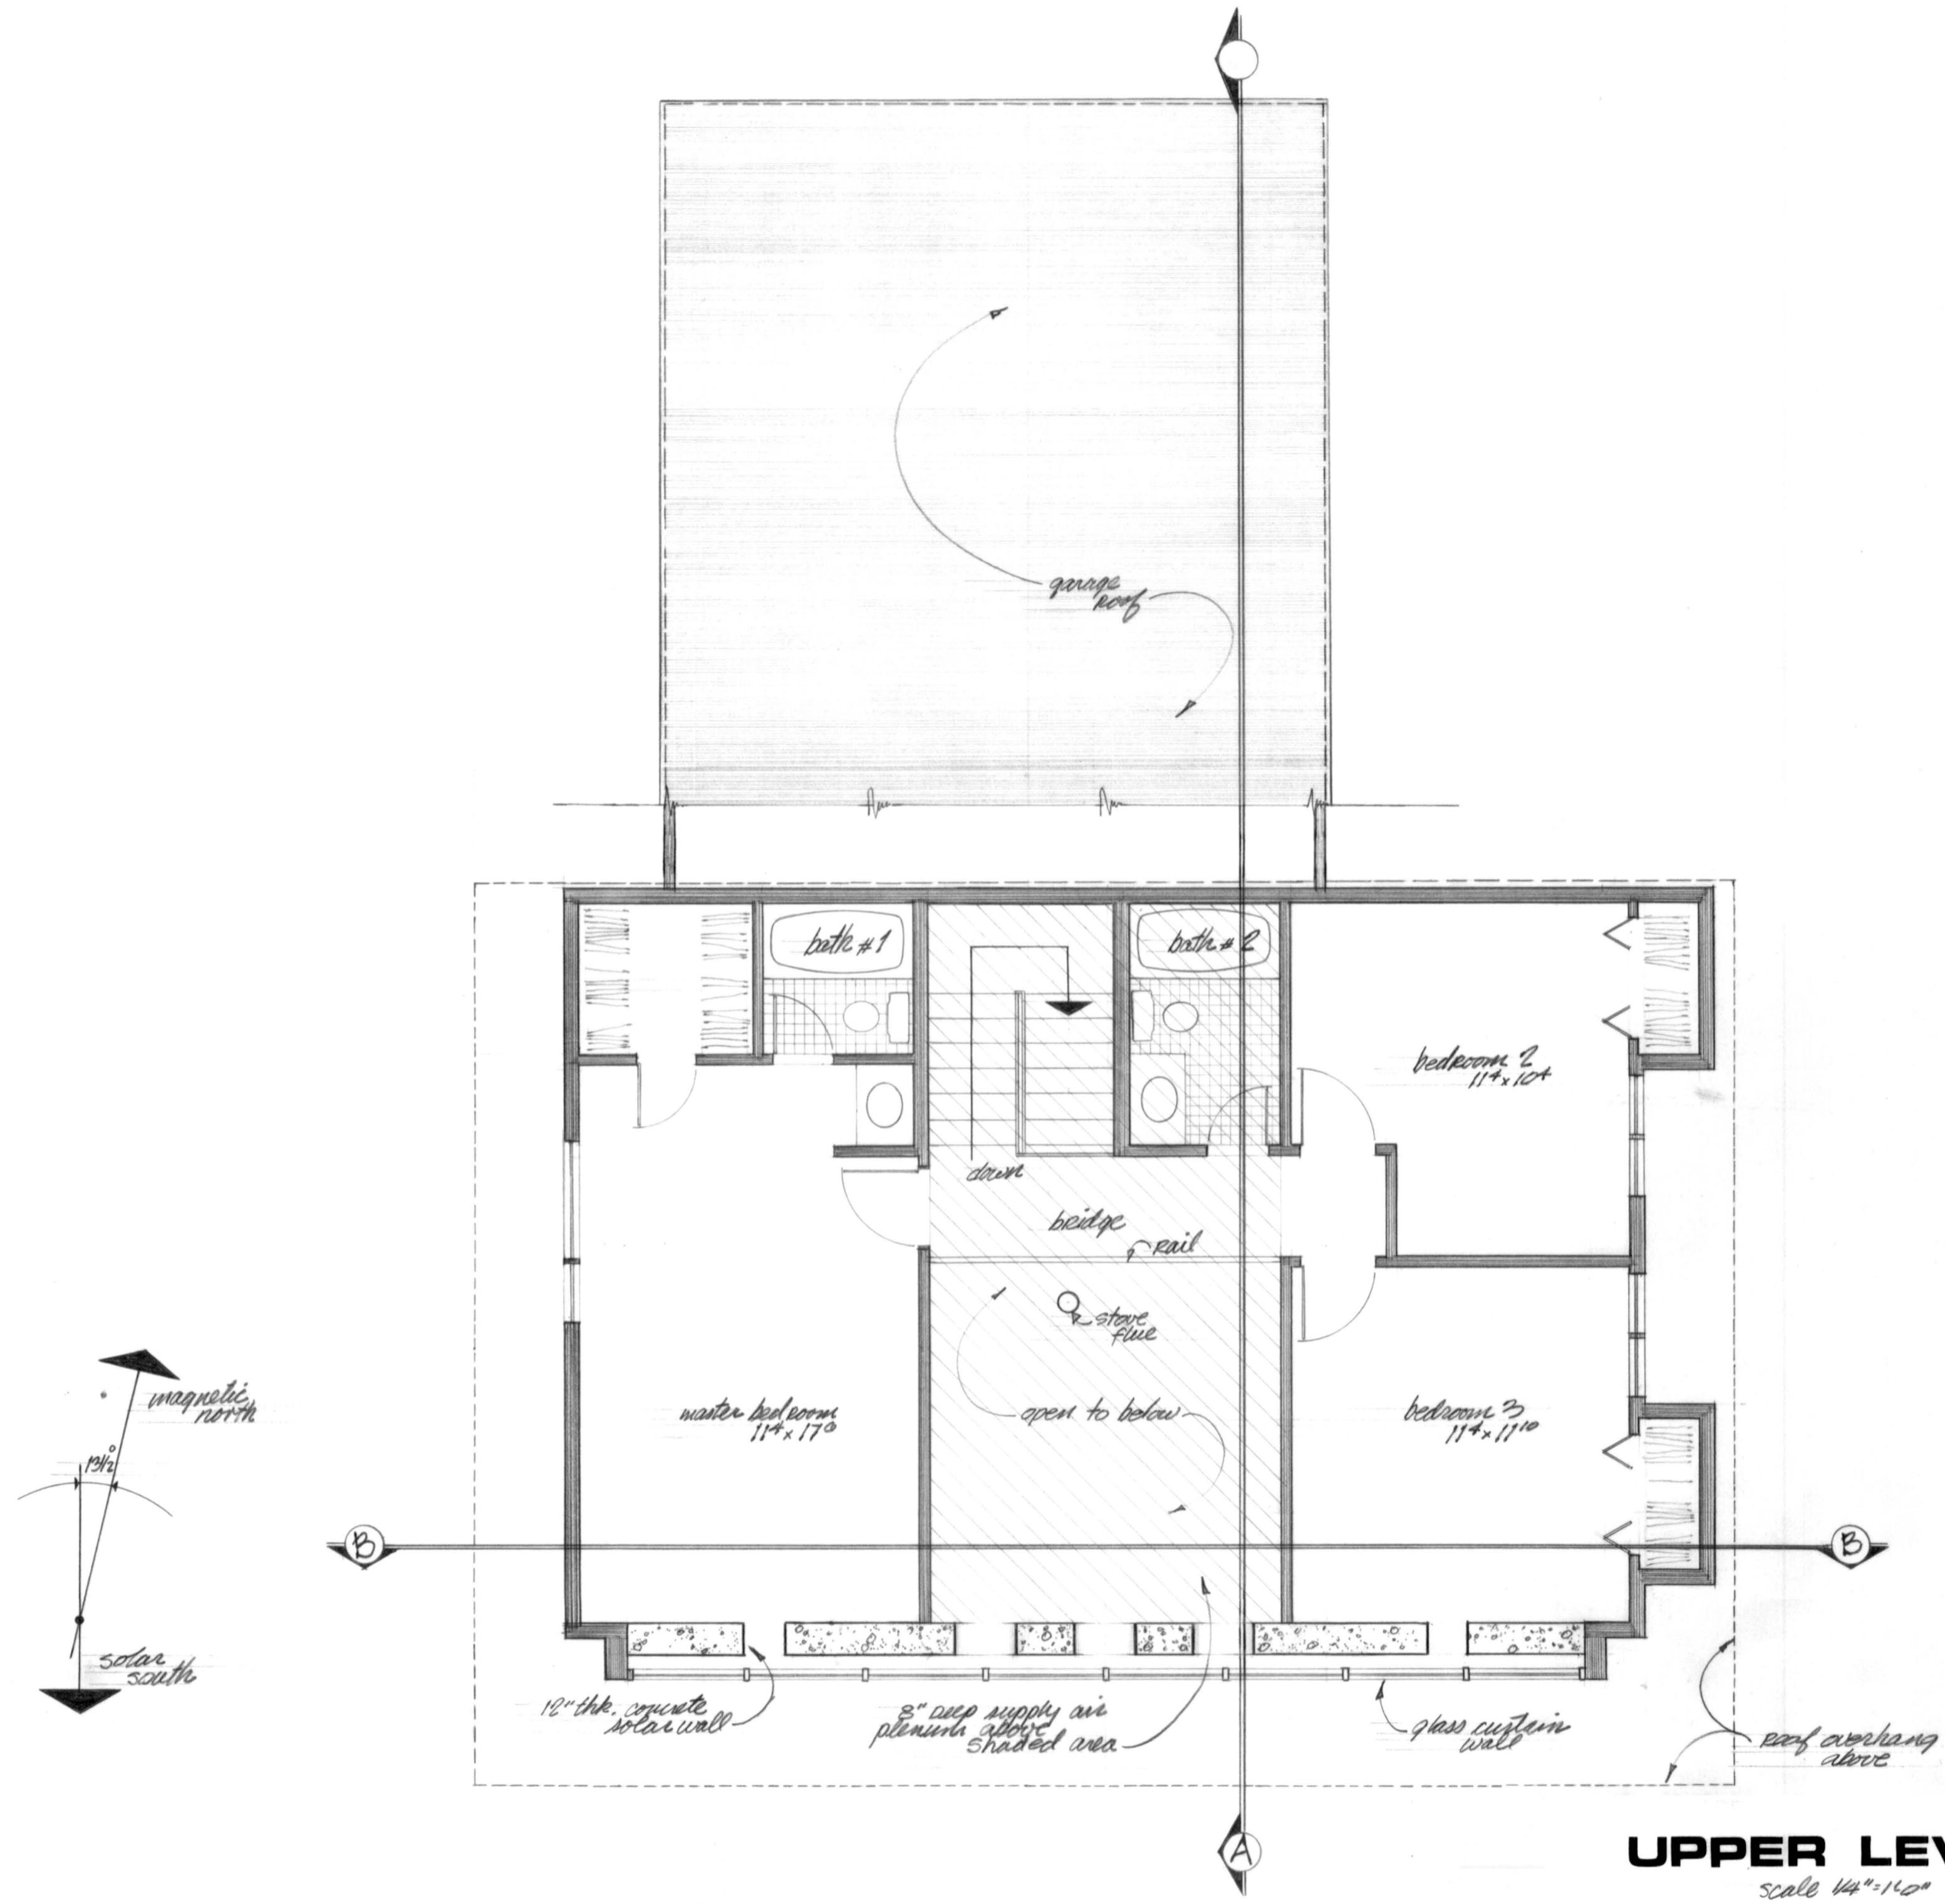


Melton




EAST ELEVATION

scale: 1/4"=1'-0"

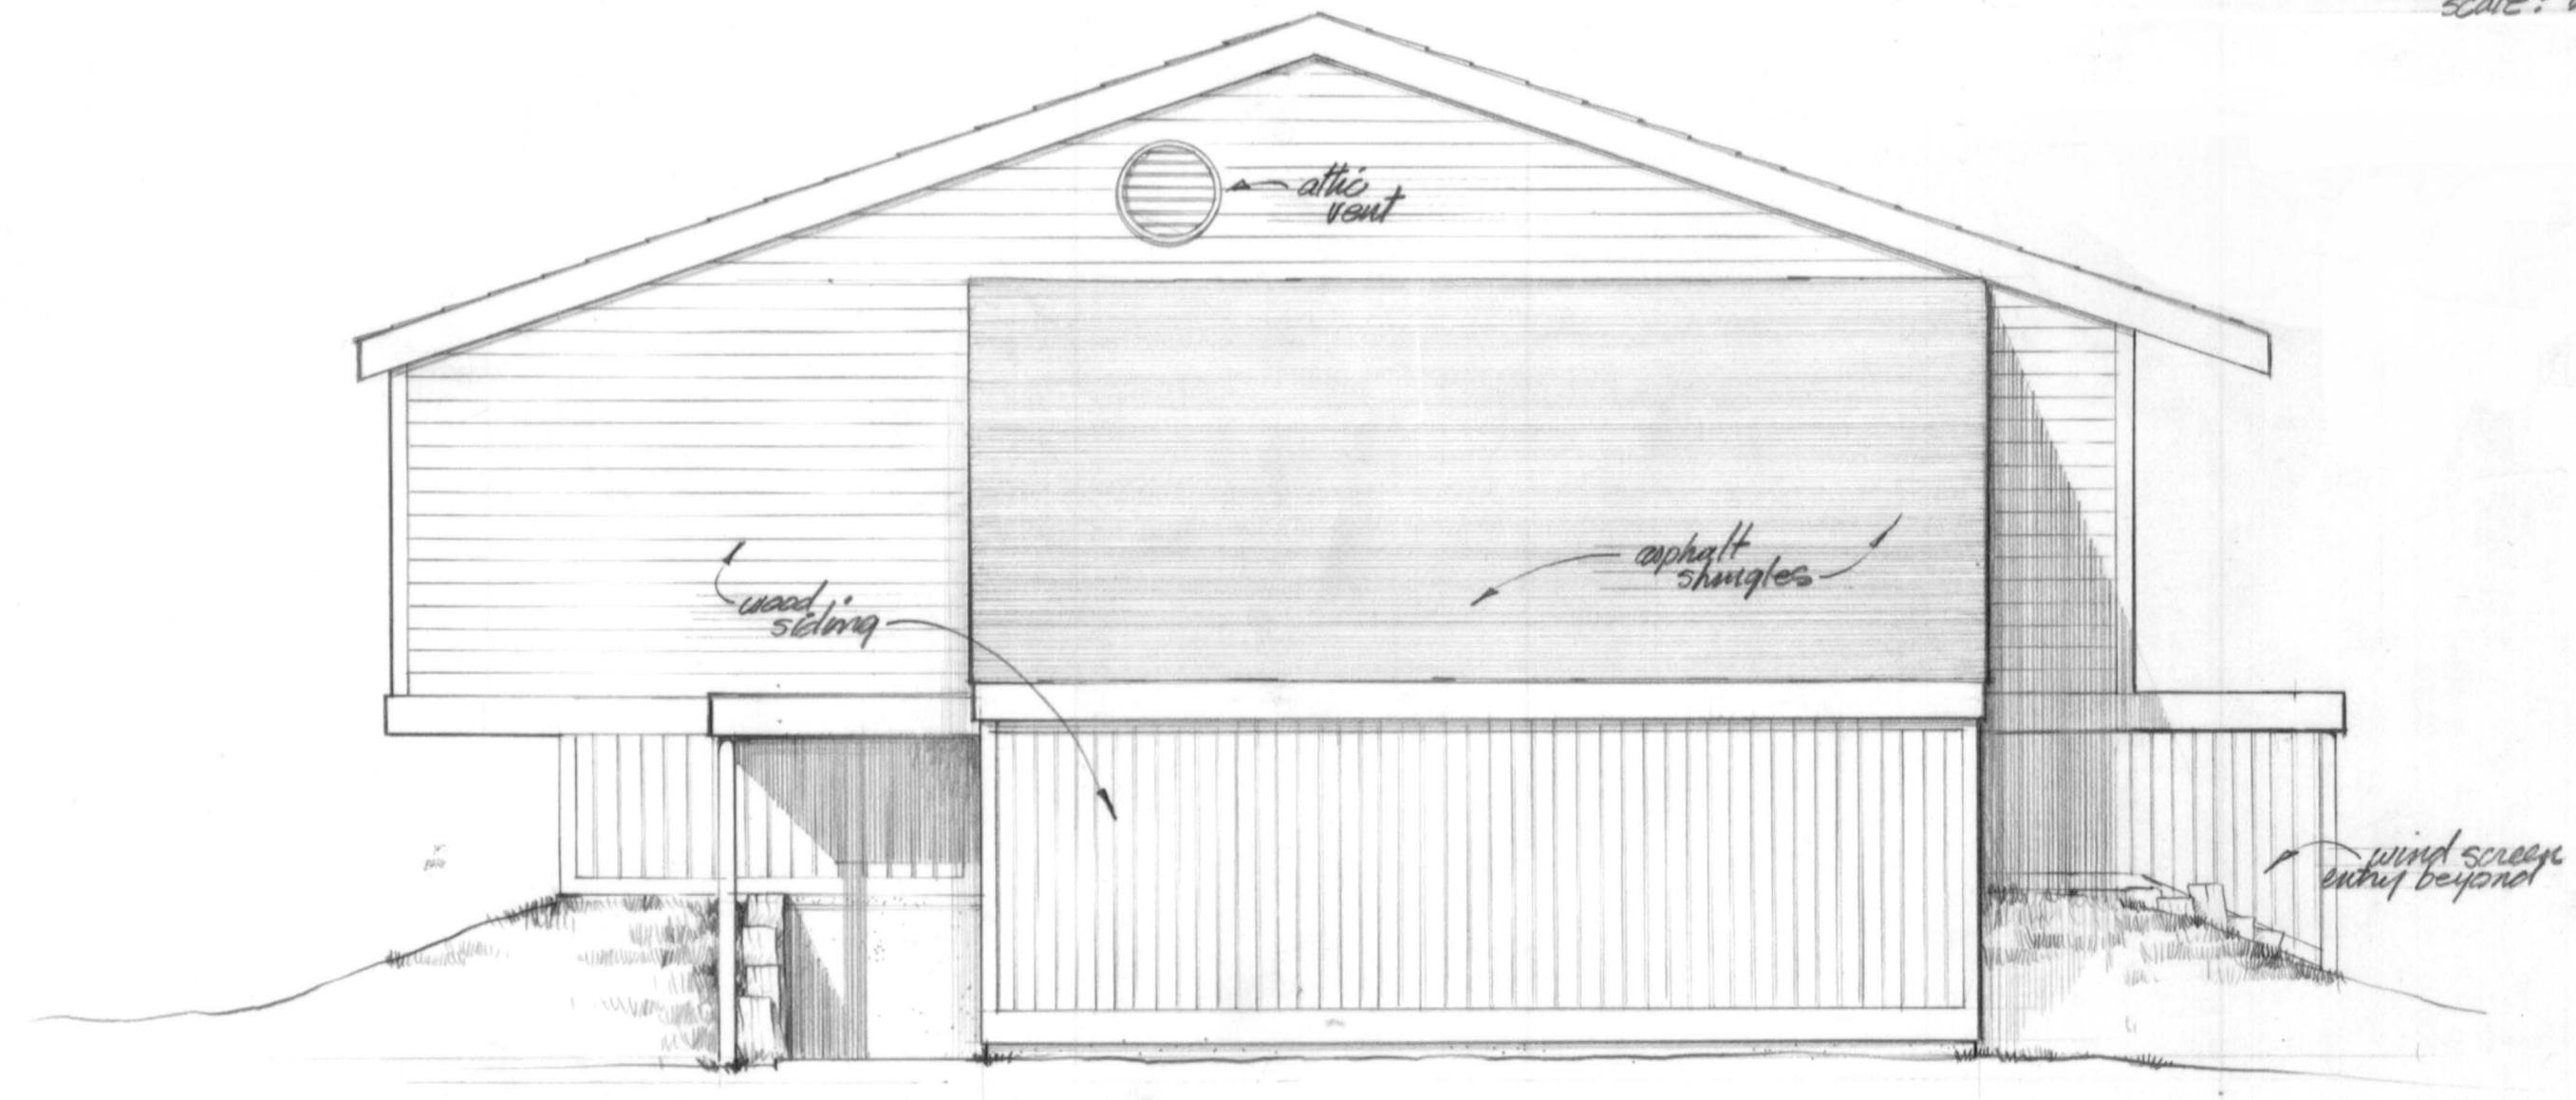


NORTH ELEVATION

scale: 1/4"=1'-0"

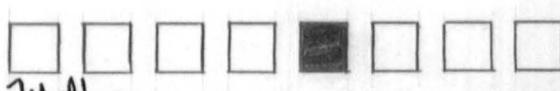


Wetton

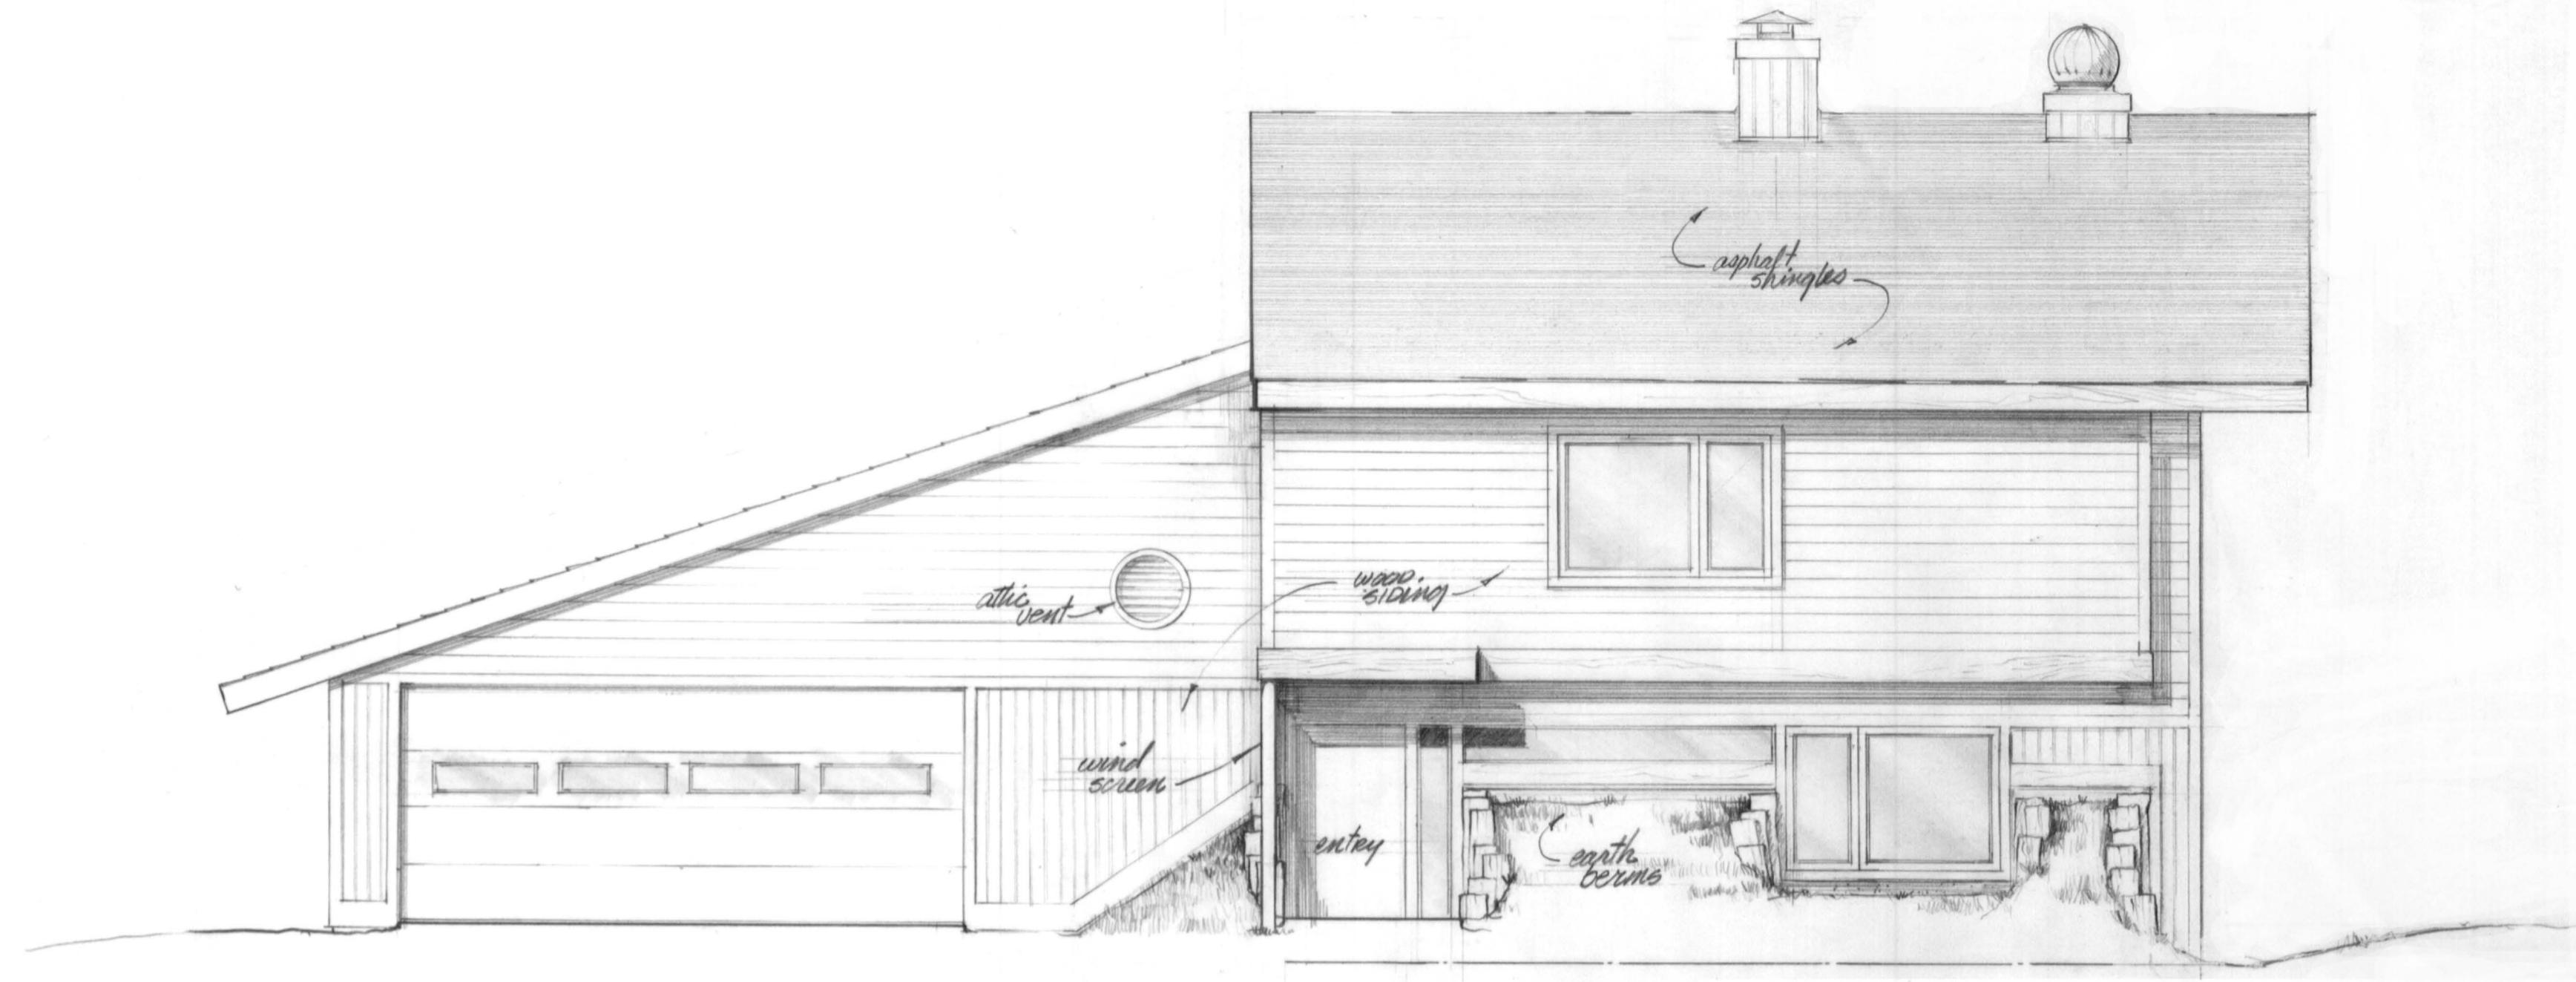

WEST ELEVATION

scale. 144"-10"

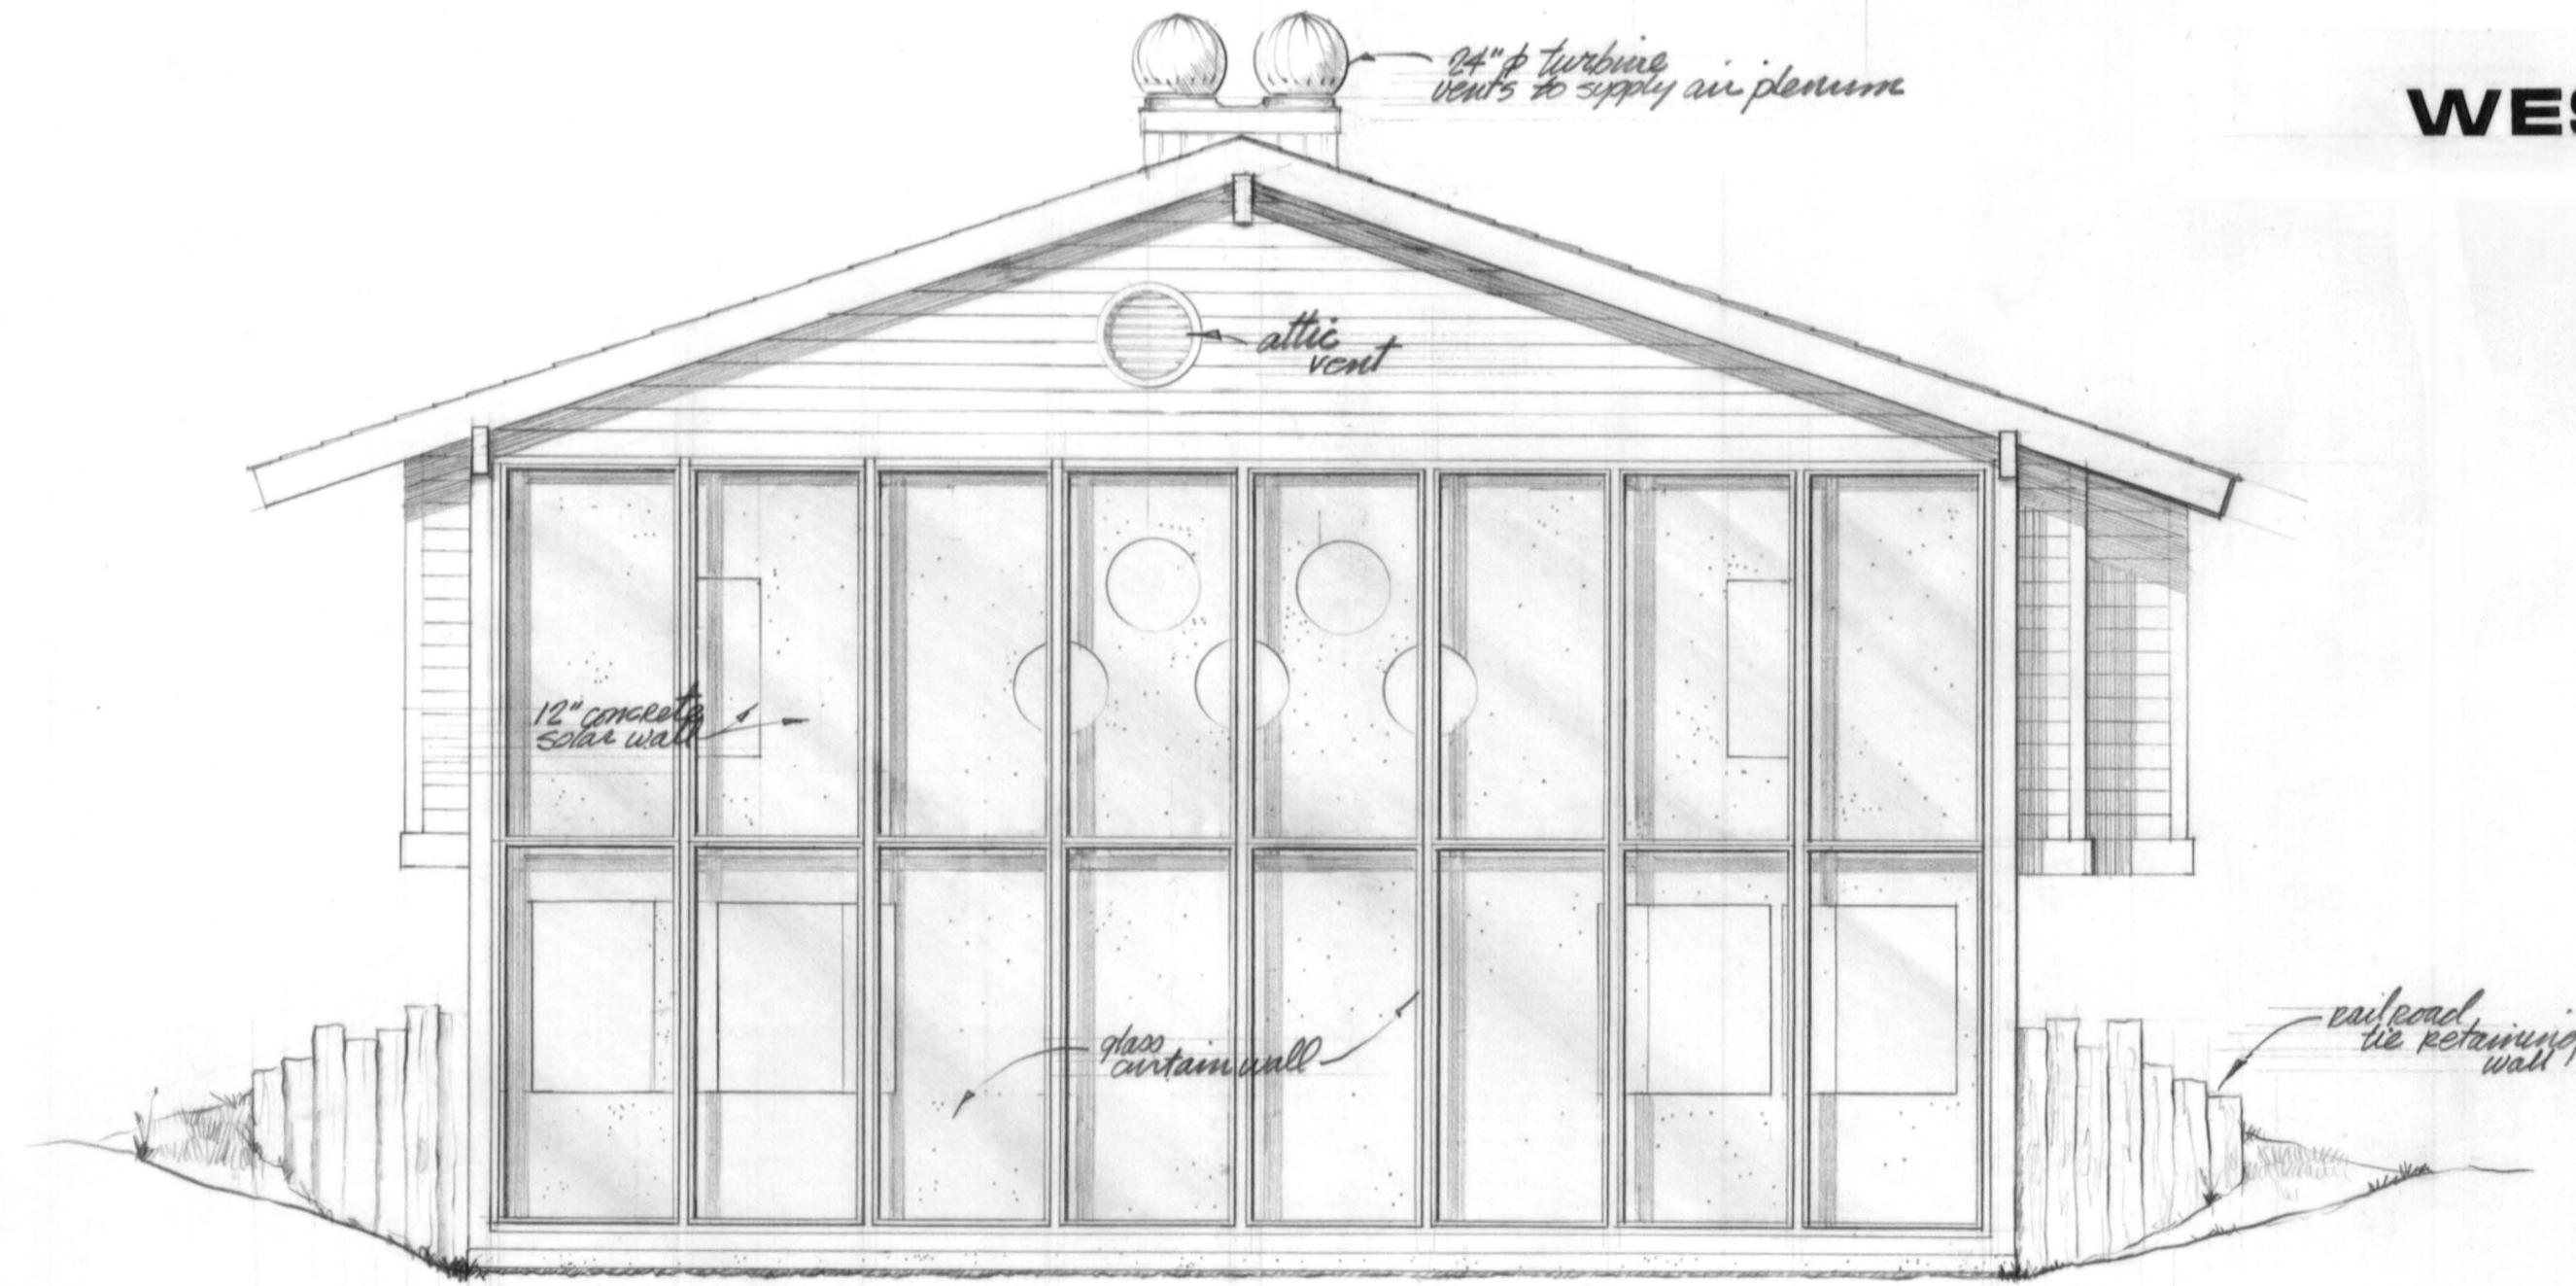

SOUTH ELEVATION

scale. 144"-10"

